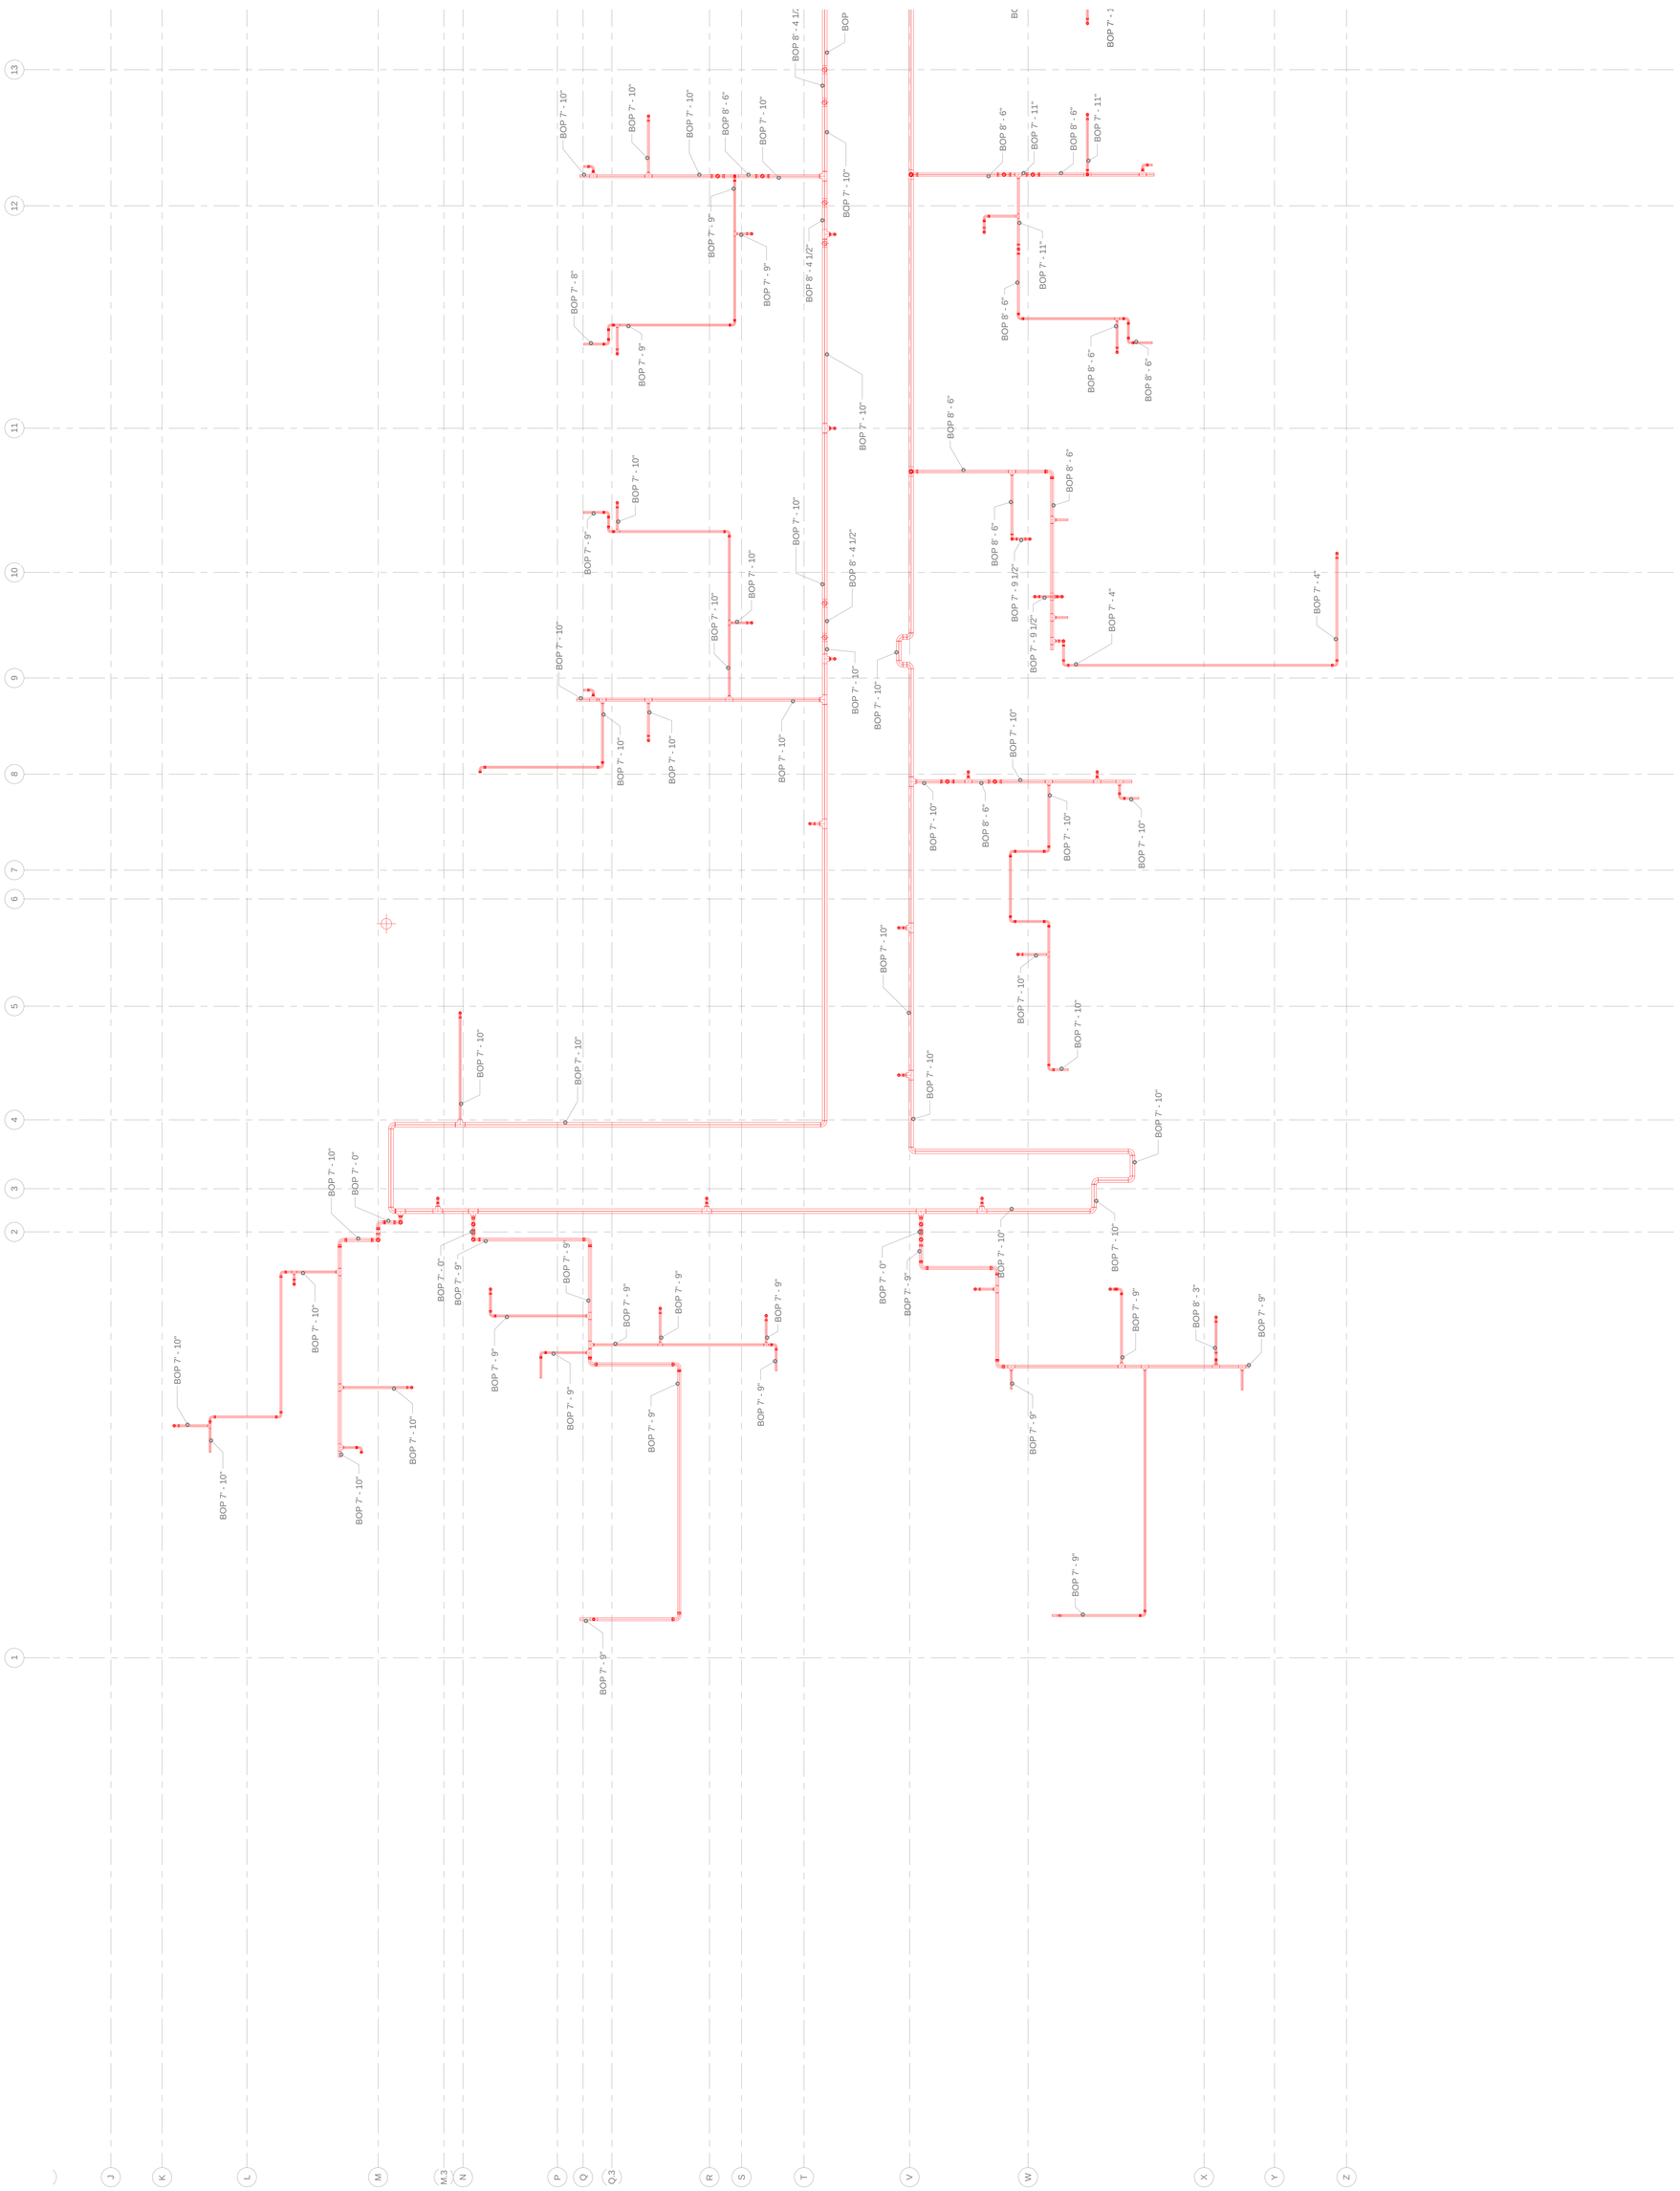

NO	DATE	DESC

REVISIONS

ARCHITECTURE	A:192.192.192
STRUCTURE	S:147.182.255
HVAC	R:255.128.064
FIRE PROTECTION	F:128.000.128
ELECTRICAL	E:255.128.064
PLUMBING	P:000.000.128
TOCCI BUILDING CORP	

PRJ MGR	PMT
SUPER	JA
BIM LEAD	JV
OAGC	JV
PROJECT NO	13-381
ISSUED	2015.09.14

HOMEWOOD SUITES

111 BOYLSTON STREET
BROOKLINE, MA

660 Main Street
Woburn MA 01801
P: 781.935.5500
F:781.935.1888

TOCCI

SDC-5.4 -5L

FP COORDINATION

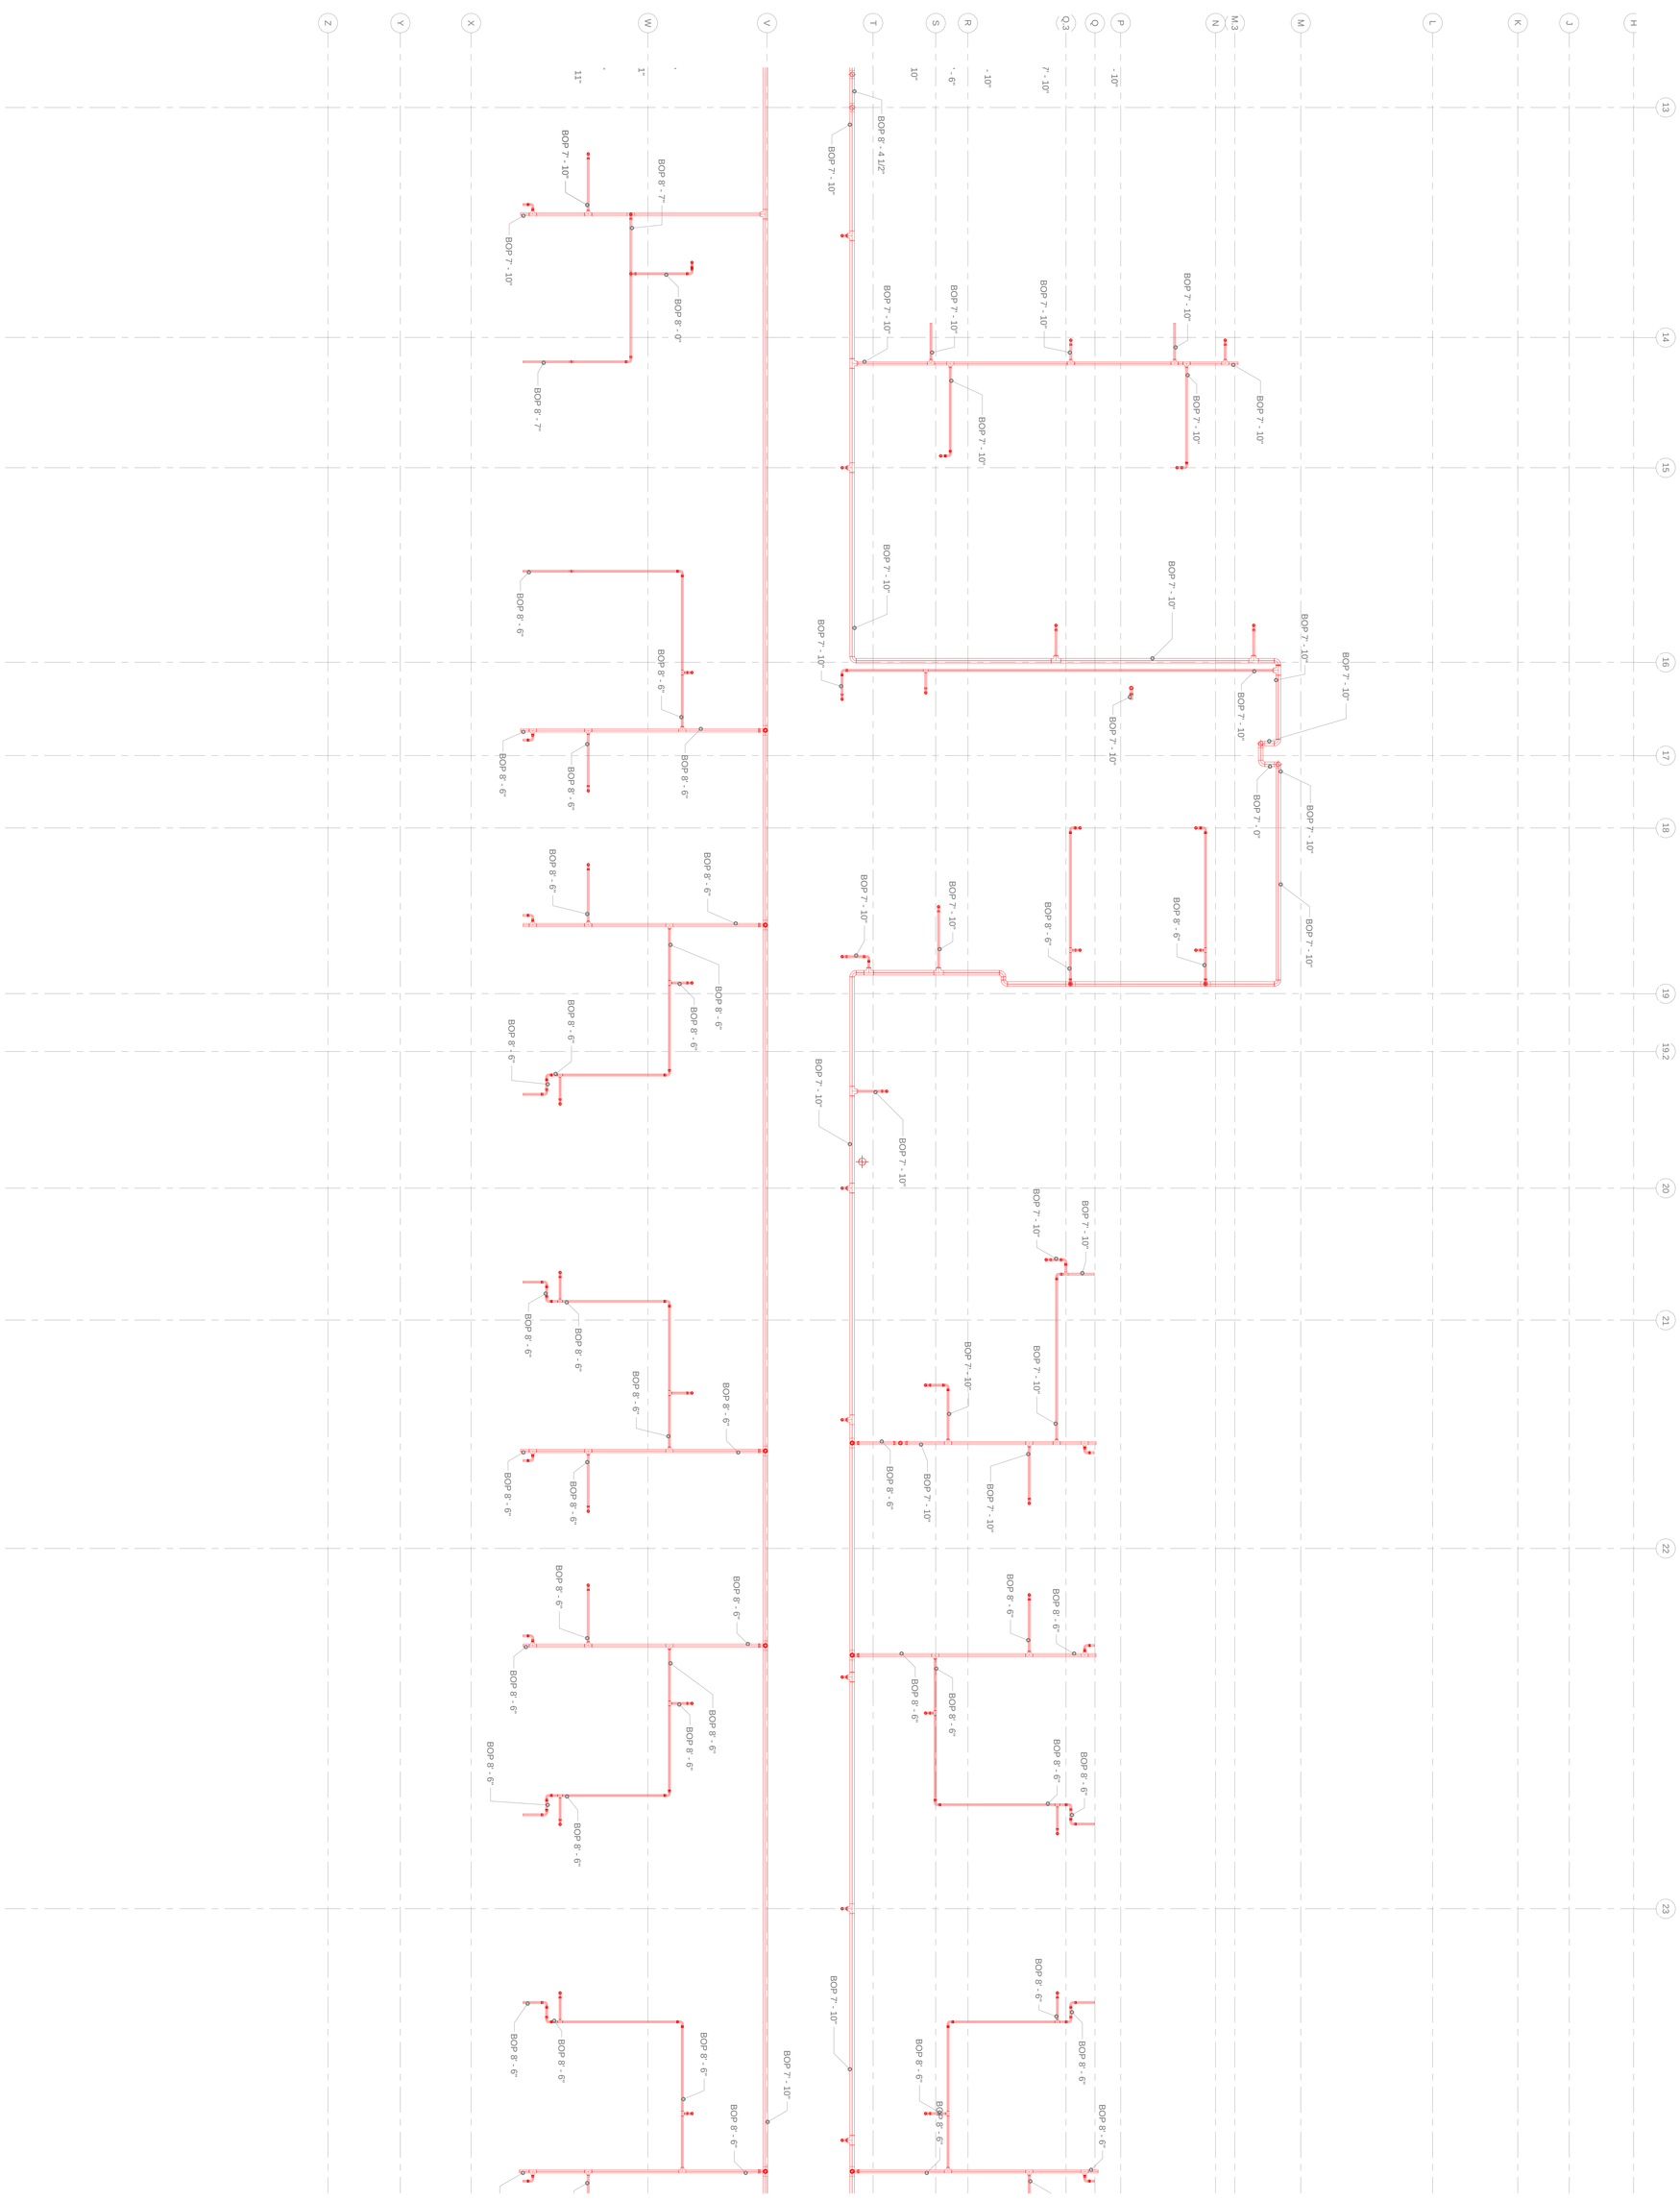

660 Main Street
Woburn MA 01801
P: 781.935.5500
F:781.935.1888

HOMEWOOD SUITES

111 BOYLSTON STREET
BROOKLINE, MA

PRJ MGR	PMT
SUPER	JA
BIM LEAD	JV
QAQC	JV
PROJECT NO	13-381
ISSUED	2015.09.14

REVISIONS		
NO	DATE	DESC

A:192.192.192	S:147.182.255	H:002.128.064	F:255.000.000	E:255.128.064	P:000.255.127	
ARCHITECTURE	STRUCTURE	HVAC	FIRE PROTECTION	ELECTRICAL	PLUMBING	TOCCI BUILDING CORP

SDC-5.5 -5L

FP COORDINATION

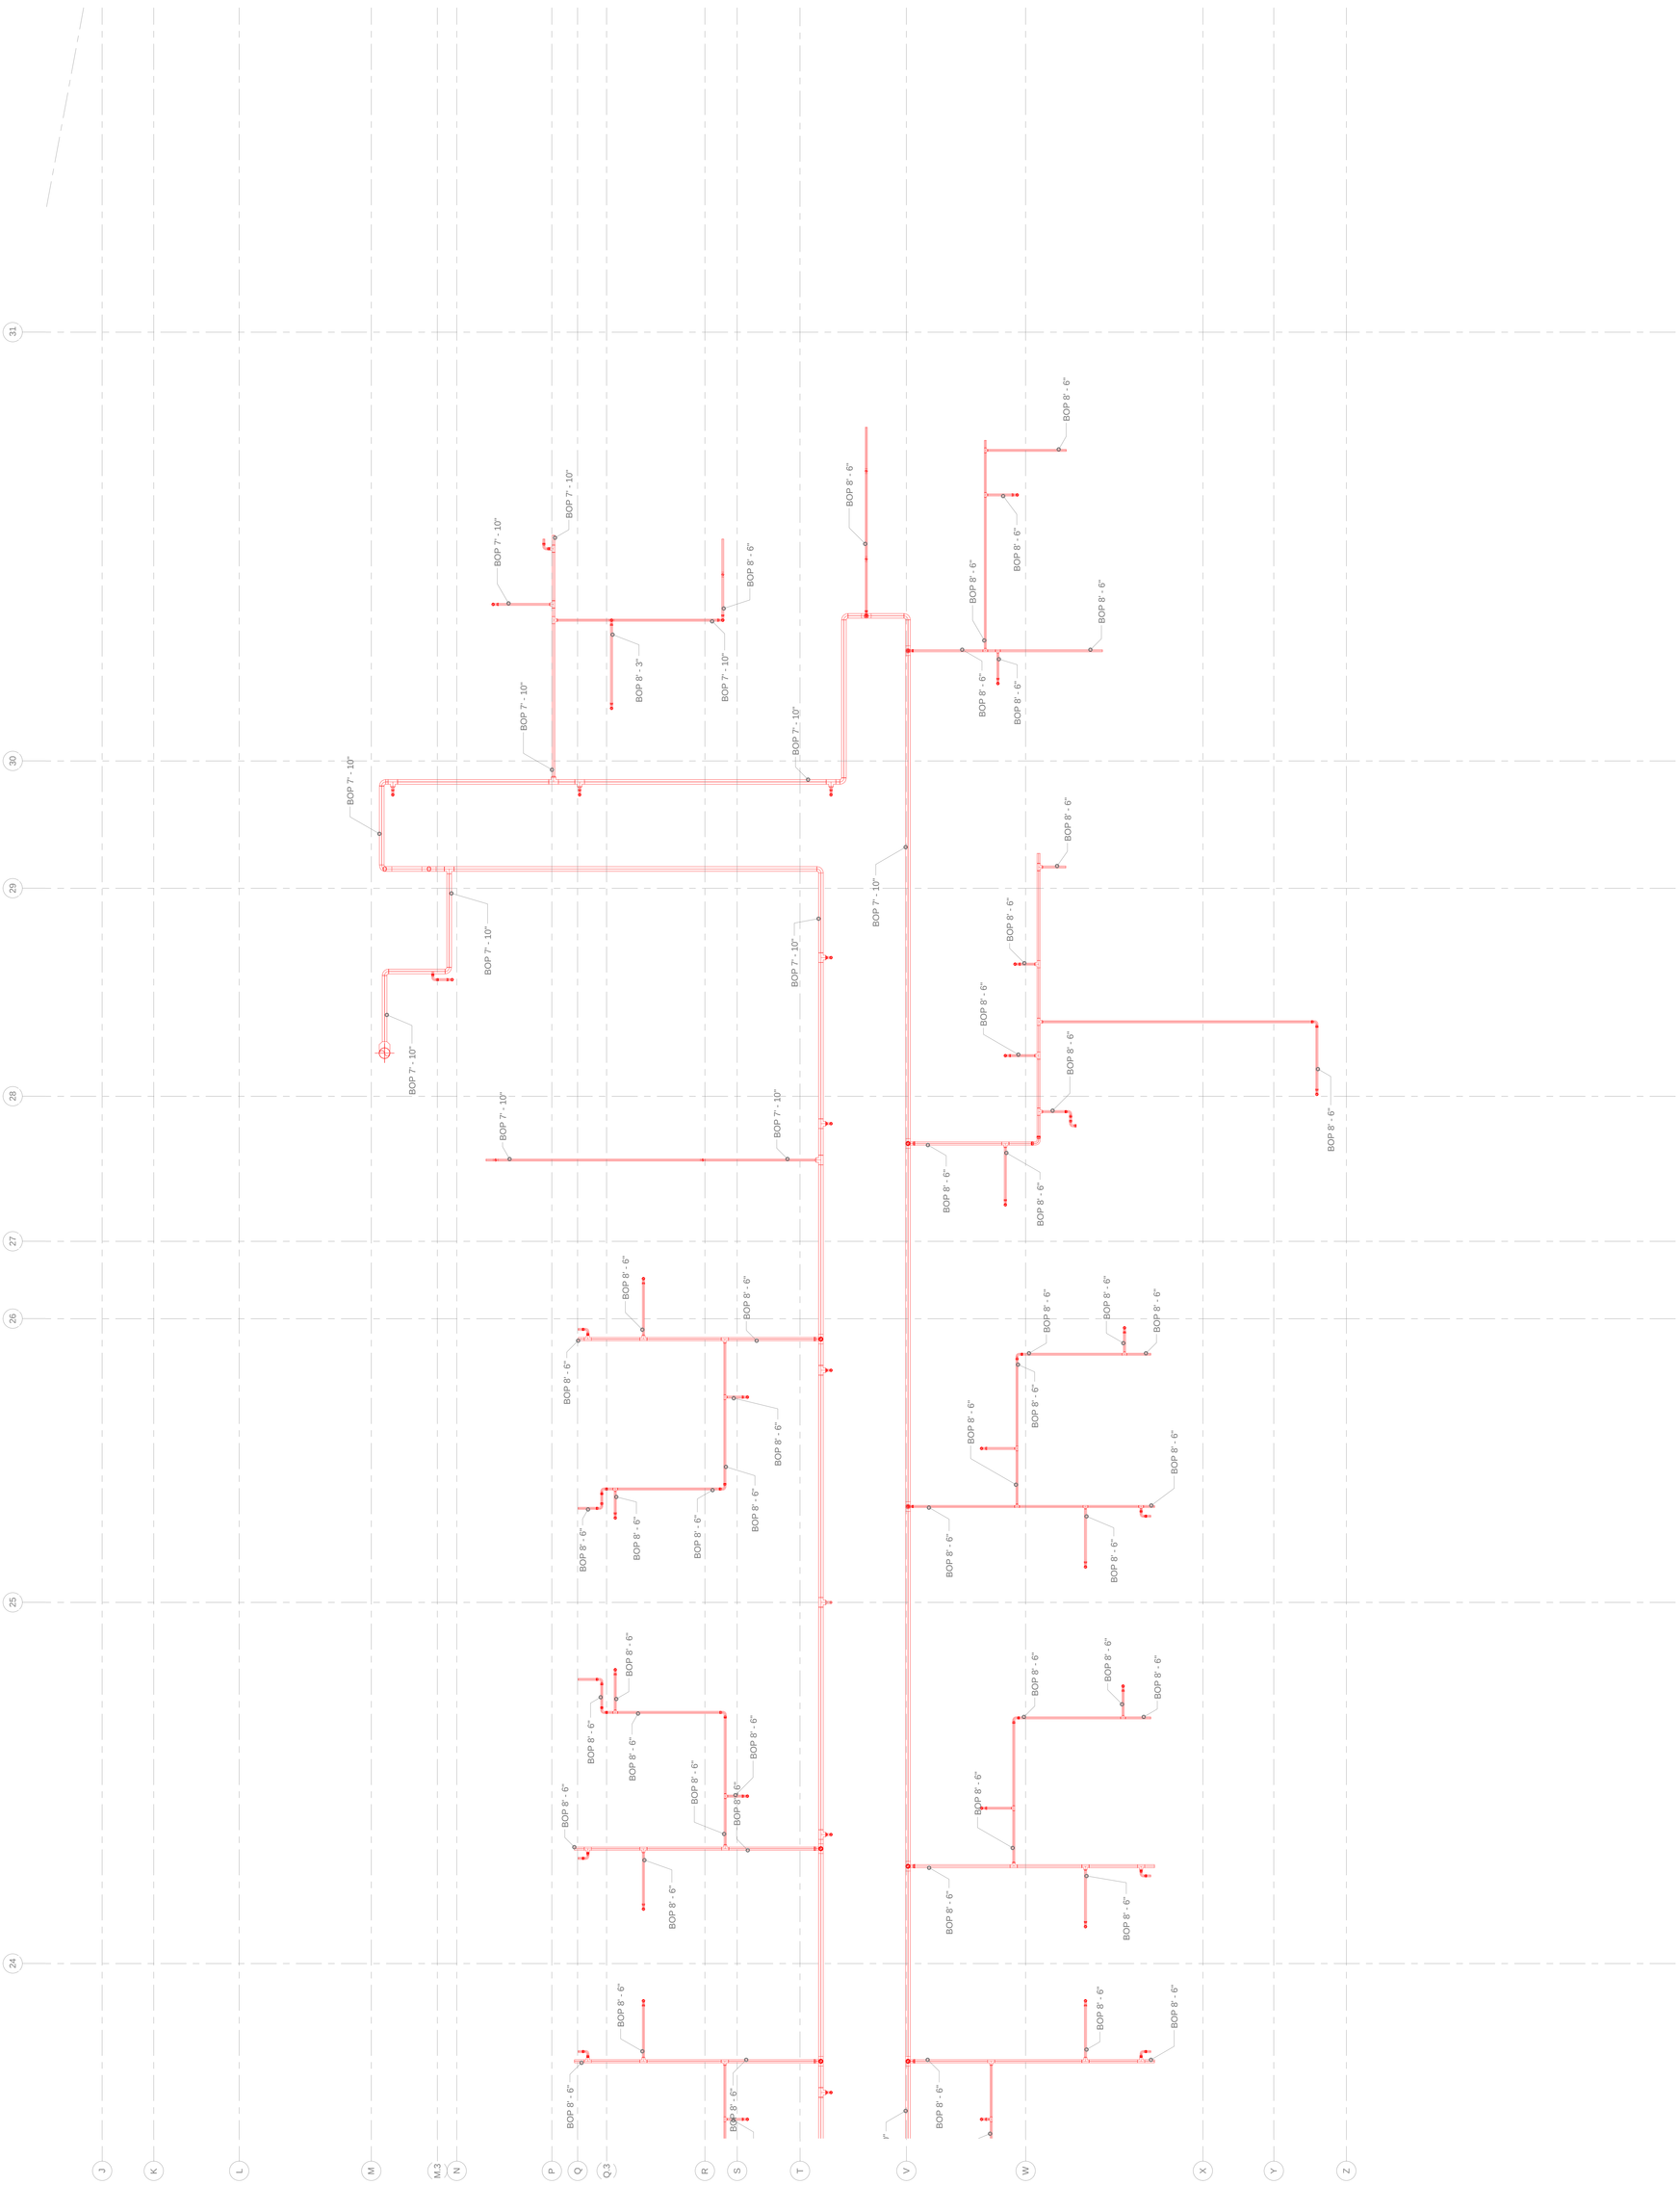

660 Main Street
Woburn MA 01801
P: 781.935.5500
F:781.935.1888

HOMEWOOD SUITES

111 BOYLSTON STREET
BROOKLINE, MA

PRJ MGR	PMT
SUPER	JA
BIM LEAD	JV
QAQC	JV
PROJECT NO	13-381
ISSUED	2015.09.14

NO	DATE	DESC
REVISIONS		

ARCHITECTURE	A:192.192.192
STRUCTURE	S:147.182.255
HVAC	H:255.128.254
FIRE PROTECTION	F:128.128.128
ELECTRICAL	E:255.128.064
PLUMBING	P:000.000.127

TOCCI BUILDING CORP

SDC-5.6 -5L

FP COORDINATION